




TOWN OF HARVARD, MASSACHUSETTS
HARVARD-DEVENS WATER SYSTEM
INTERCONNECTION PROJECT
CONTRACT NO. 1 / DWSRF 7285
PERMIT DRAWINGS
DECEMBER 2023

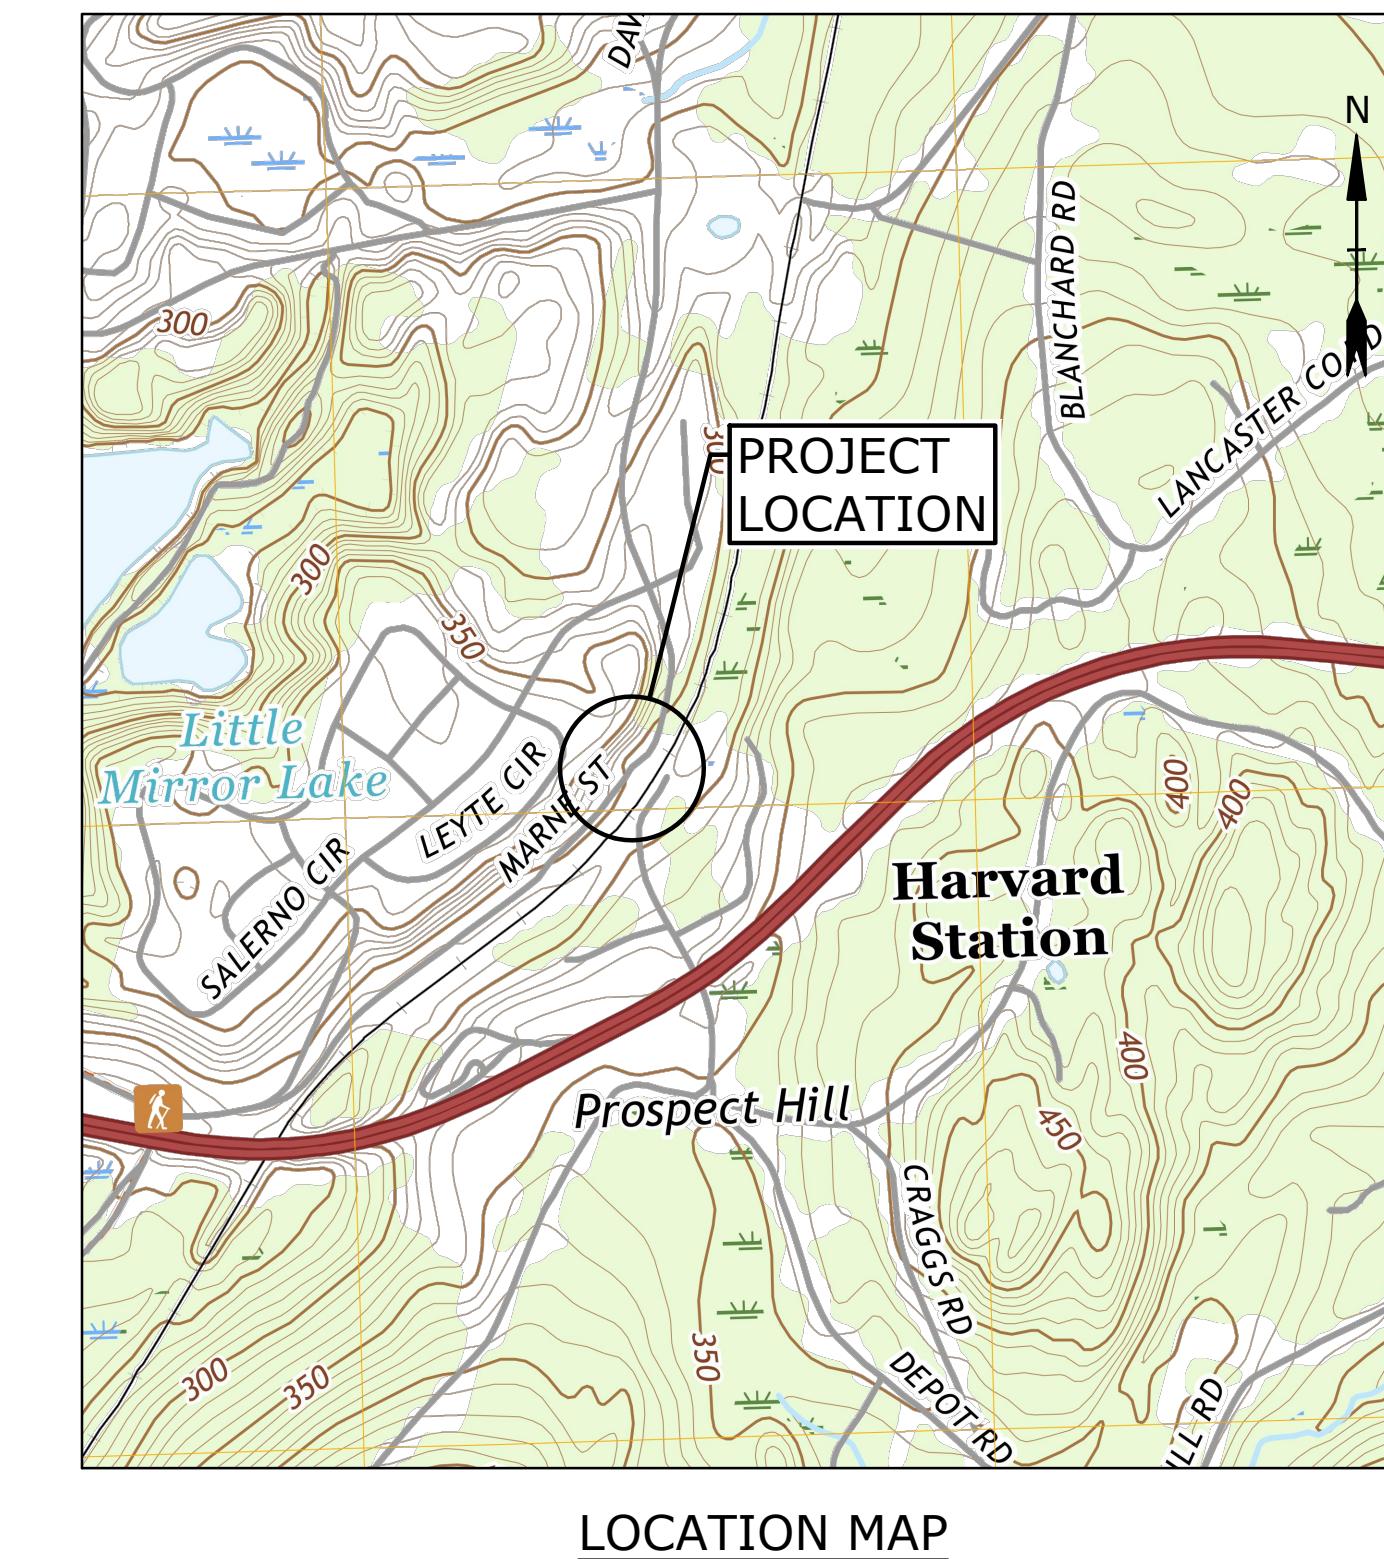

PREPARED BY:
Tighe&Bond

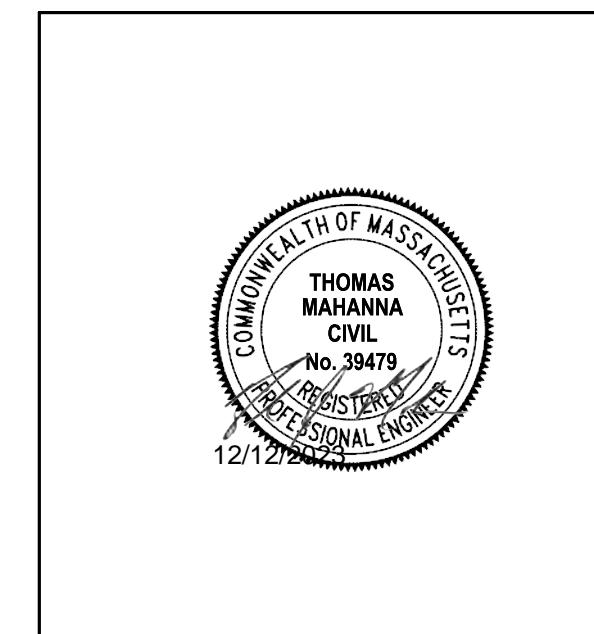

THOMAS J. MAHANNA, PE

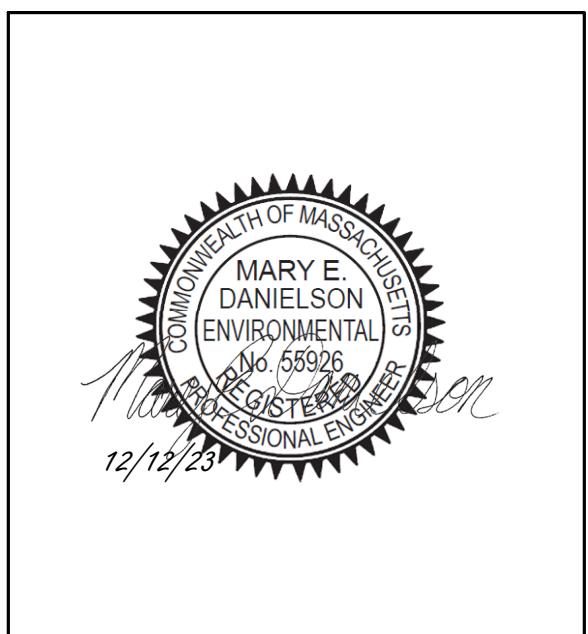

MARY E. DANIELSON, PE

PREPARED FOR:
TOWN OF HARVARD


DEPARTMENT OF PUBLIC WORKS
TIM KILHART - DIRECTOR

TOWN ADMINISTRATOR
TIMOTHY BRAGAN

WATER AND SEWER COMMISSIONERS
CINDY RUSSO - CHAIR
RICHARD MAIORE
KYLE HEDRICK

THIS DOCUMENT IS RELEASED
TEMPORARILY FOR PROGRESS REVIEW ONLY.
IT IS NOT INTENDED FOR BIDDING OR
CONSTRUCTION PURPOSES.

COMPLETE SET 41 SHEETS

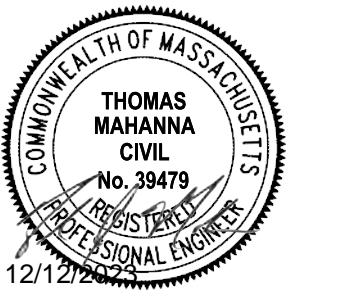

PERMIT DRAWINGS - NOT FOR CONSTRUCTION

THIS DOCUMENT IS INCOMPLETE AND IS
RELEASED TEMPORARILY FOR PROGRESS
REVIEW ONLY. IT IS NOT INTENDED FOR
BIDDING OR CONSTRUCTION PURPOSES.

Harvard-Devens Water System Interconnection Project

Harvard Public
Works
Department

Harvard,
Massachusetts

MARK	DATE	DESCRIPTION
PROJECT NO.:	H1776-016	
DATE:	DECEMBER 2023	
FILE:	H1776-16-C-100.dwg	
DRAWN BY:	TAL	
DESIGNED/CHECKED BY:	JEC	
APPROVED BY:	TJM	


EXISTING CONDITIONS AND EROSION CONTROL PLAN


SCALE:	AS SHOWN
SCALE:	0 15' 30'

C-100

DEVENS ENTERPRISE COMMISSION ENDORSEMENT
SIGNATURE: _____
DATE: _____
TITLE: _____

ADDRESS:
39 SHERIDAN ROAD
DEVENS ASSESSMENT PARCEL ID: 4

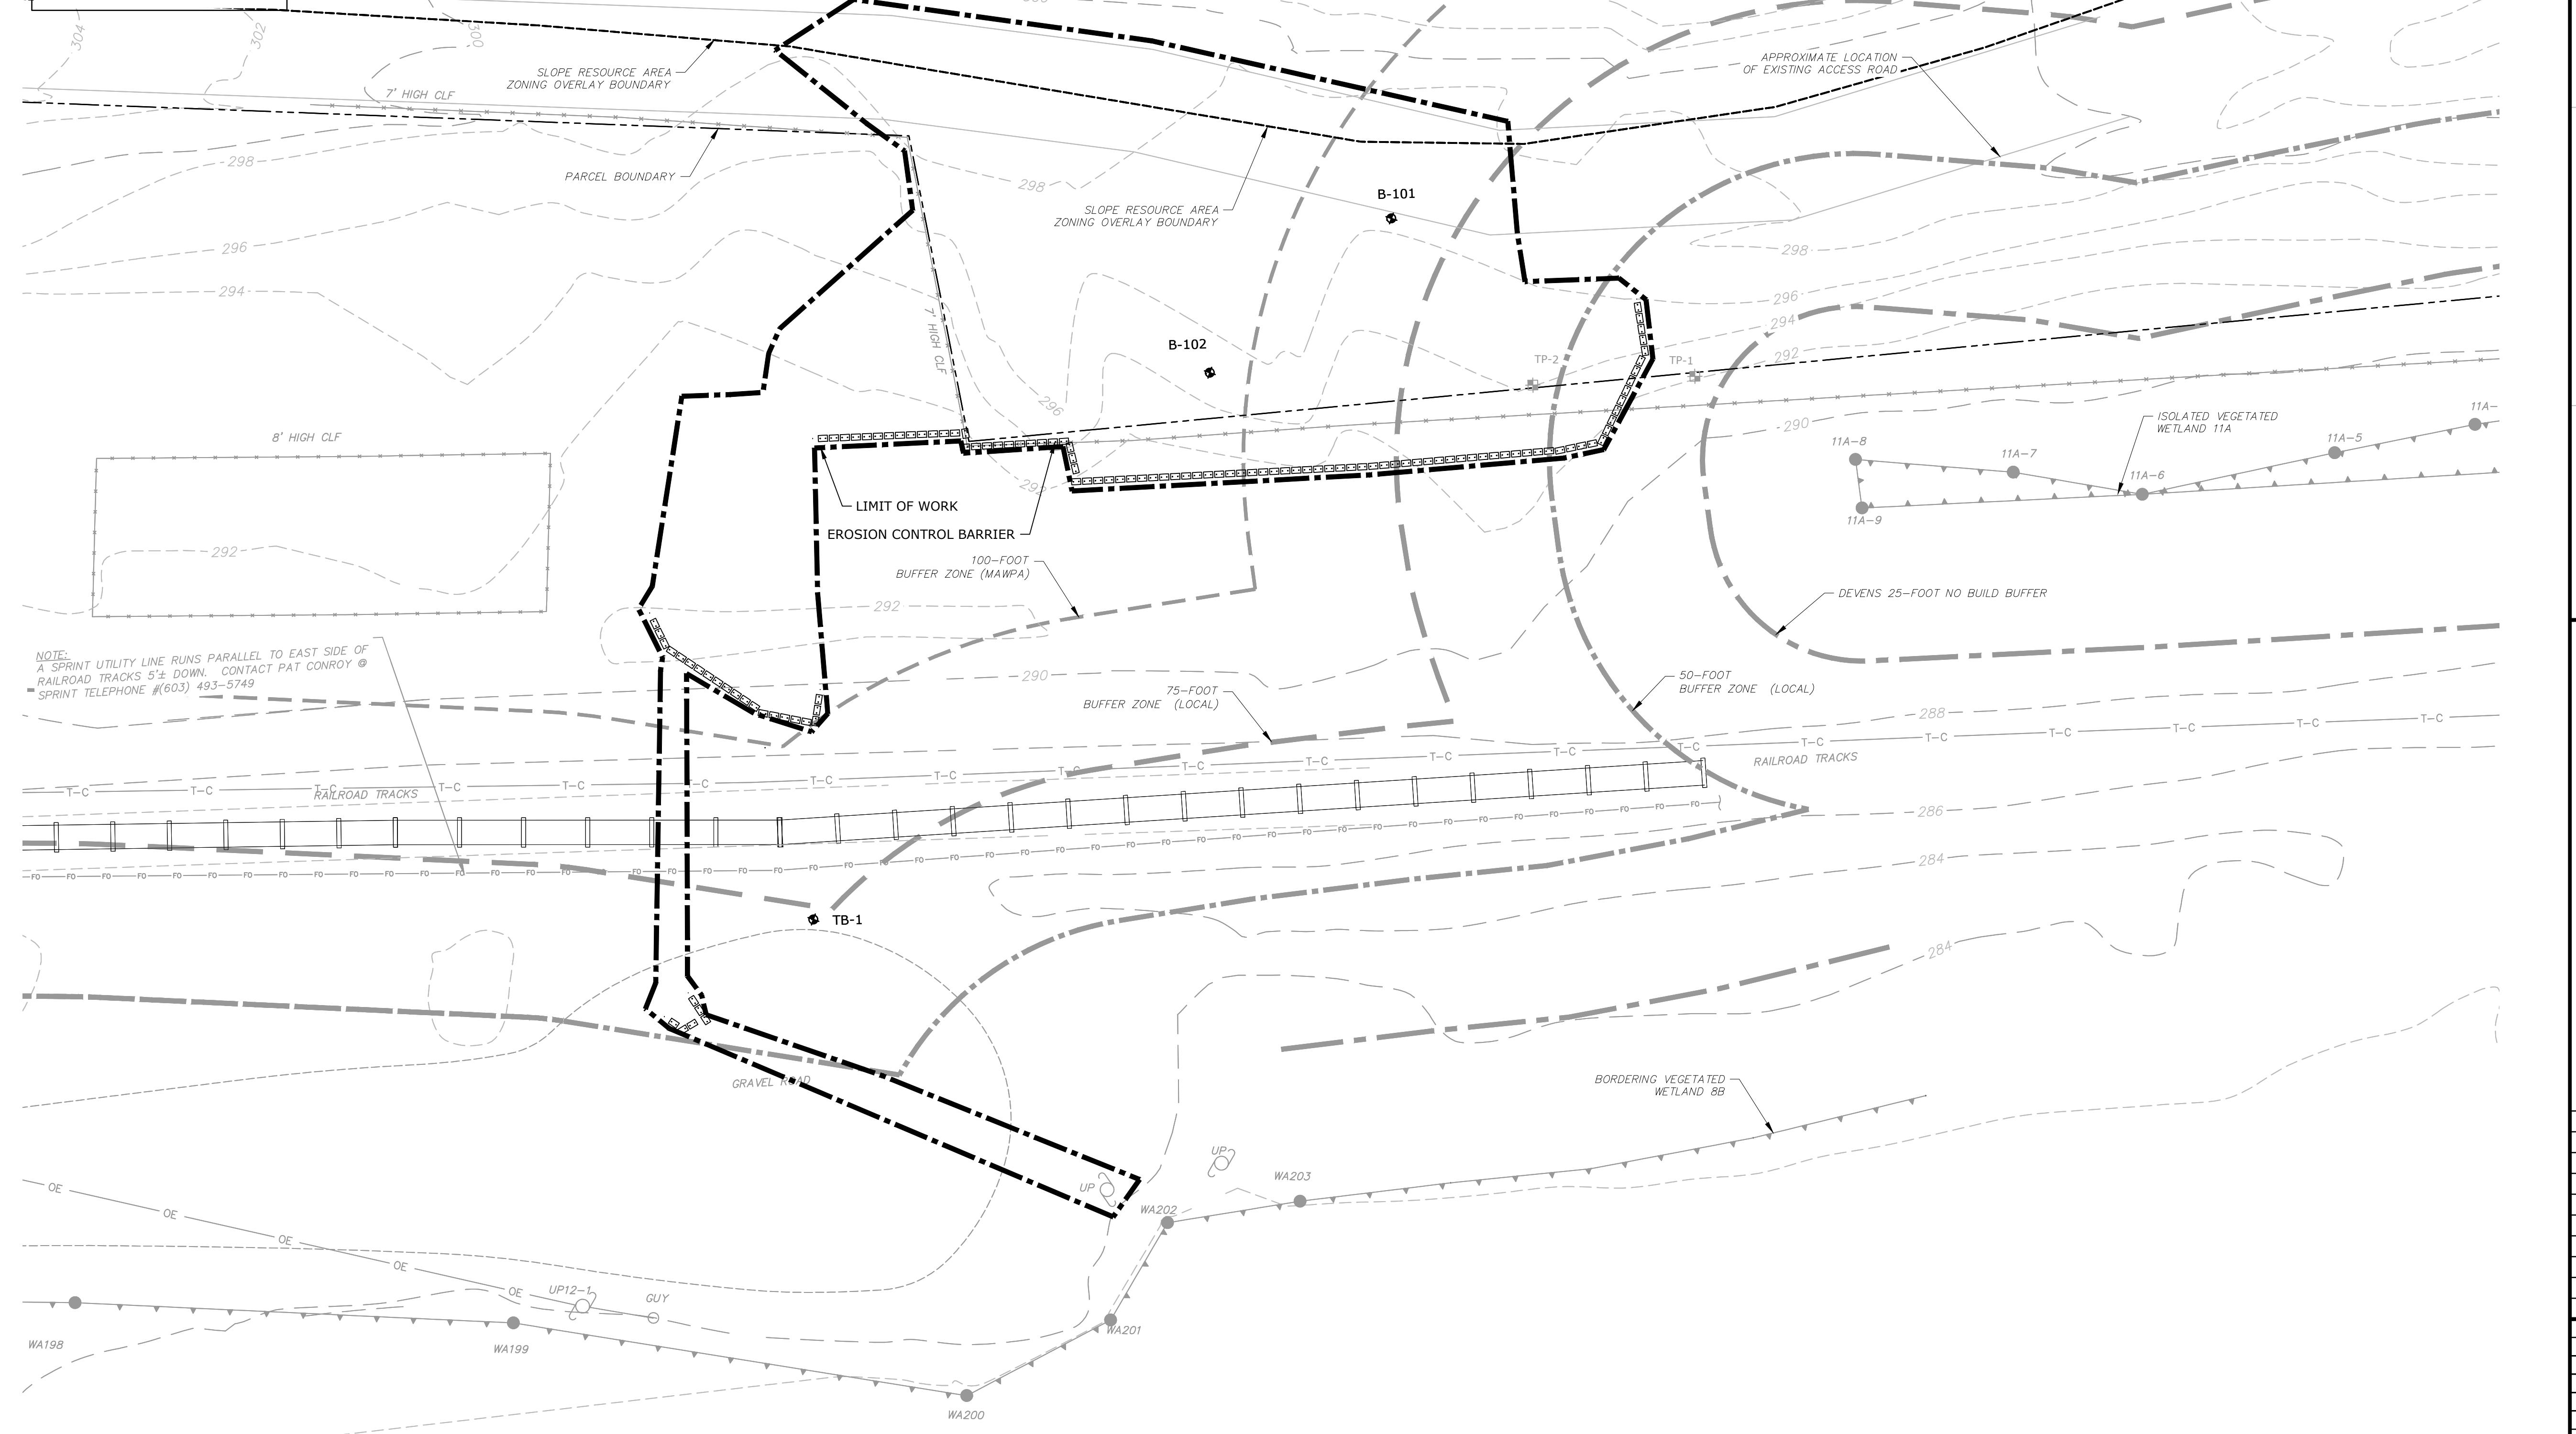

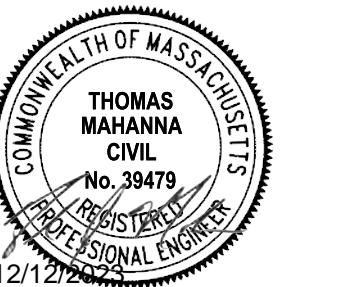

PERMIT DRAWINGS - NOT FOR CONSTRUCTION

THIS DOCUMENT IS INCOMPLETE AND IS
RELEASED TEMPORARILY FOR PROGRESS
REVIEW ONLY. IT IS NOT INTENDED FOR
BIDDING OR CONSTRUCTION PURPOSES.

Harvard-Devens Water System Interconnection Project

Harvard Public Works Department

Harvard,
Massachusetts

SETBACKS		
	REQUIRED (FT)	PROPOSED (FT)
FRONT:	25	40
SIDE:	10	6
REAR:	25	140

MARK	DATE	DESCRIPTION
PROJECT NO:		H1776-016
DATE:		DECEMBER 2023
FILE:		H1776-16-C-200.dwg
DRAWN BY:		TAL
DESIGNED/CHECKED BY:		JEC
APPROVED BY:		TJM

SITE LAYOUT PLAN


SCALE: AS SHOWN


C-200

C 300

© 2008

DEVENS ENTERPRISE COMMISSION ENDORSEMENT	
SIGNATURE:	_____
DATE:	_____
TITLE:	_____

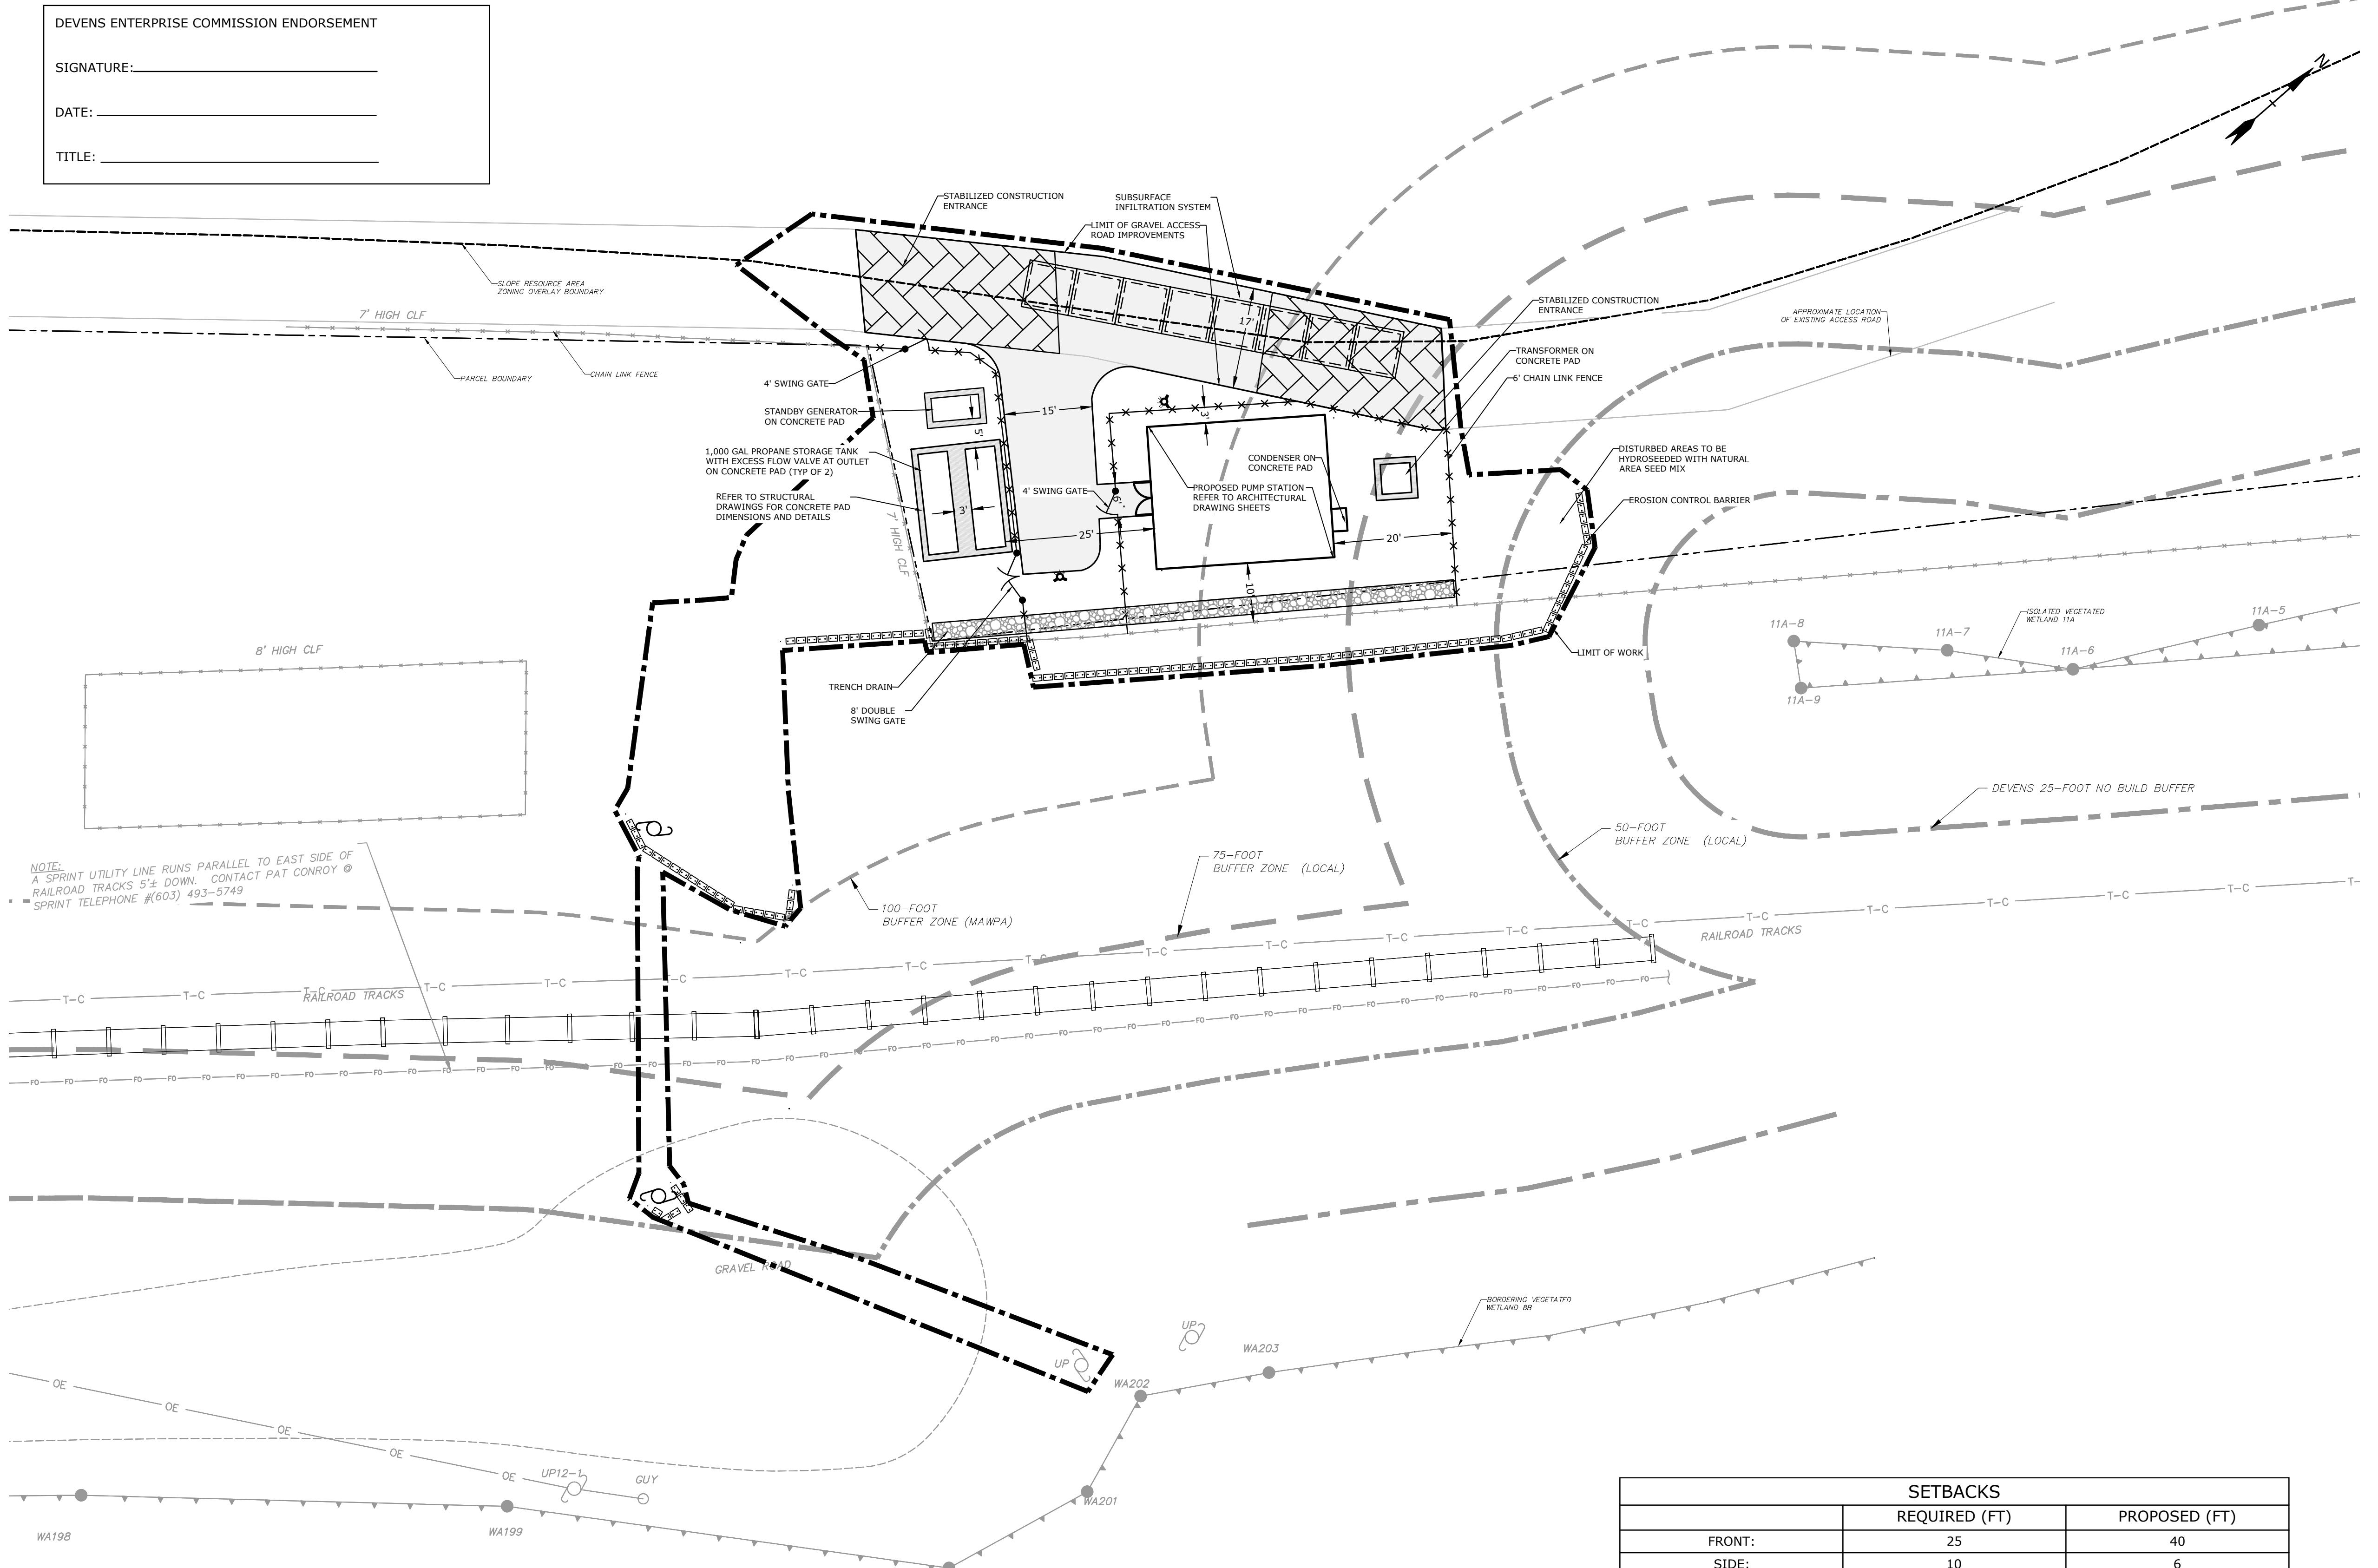

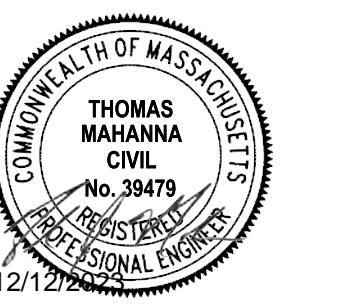

PERMIT DRAWINGS - NOT FOR CONSTRUCTION

THIS DOCUMENT IS INCOMPLETE AND IS
RELEASED TEMPORARILY FOR PROGRESS
REVIEW ONLY. IT IS NOT INTENDED FOR
BIDDING OR CONSTRUCTION PURPOSES.

Harvard-Devens Water System Interconnection Project

Harvard Public Works Department

Harvard,
Massachusetts

--	--	--

MARK	DATE	DESCRIPTION
PROJECT NO:	H1776-016	
DATE:	DECEMBER 2023	
FILE:	H1776-16-C-300.dwg	
DRAWN BY:	TAL	
DESIGNED/CHECKED BY:	JEC	
APPROVED BY:	TJM	

RADING PLAN

SCALE: AS SHOWN

C-301